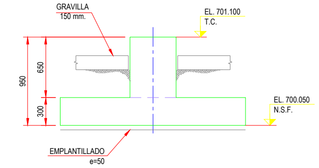

A SECCIÓN
ESCALA 1 : 25

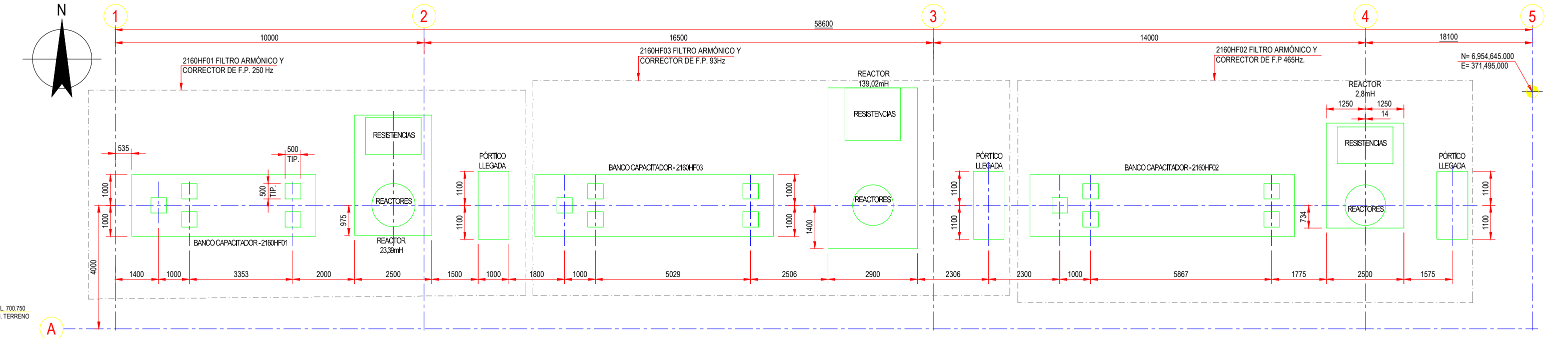

PLANTA DE FUNDACIONES
ESC. 1:125

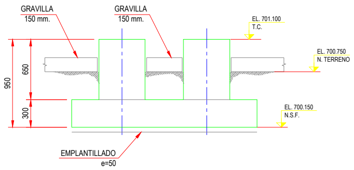

F SECCIÓN
ESCALA 1 : 25

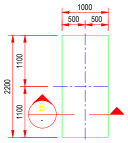

FUNDACIÓN
PÓRTICO LLEGADA
ESC. 1:50

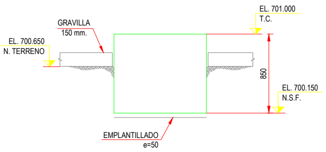

B SECCIÓN
ESCALA 1 : 25

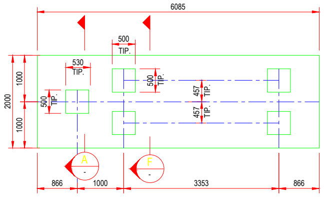

FUNDACIÓN
BANCO CAPACITADOR - 2160HF01
ESC. 1:50

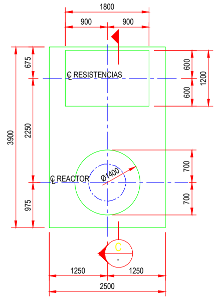

FUNDACIÓN
REACTORES Y RESISTENCIAS - 2160HF01
ESC. 1:50

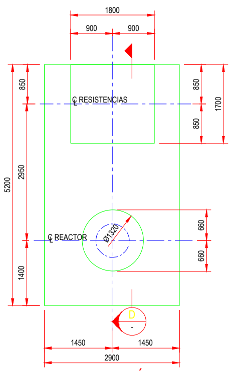

FUNDACIÓN
REACTORES Y RESISTENCIAS - 2160HF03
ESC. 1:50

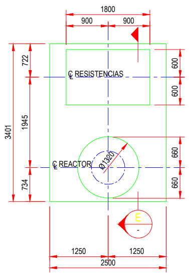

FUNDACIÓN
REACTORES Y RESISTENCIAS - 2160HF02
ESC. 1:50

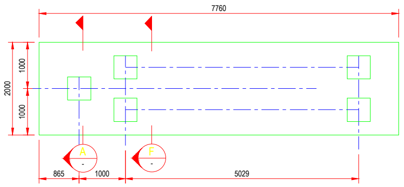

FUNDACIÓN
BANCO CAPACITADOR - 2160HF03
ESC. 1:50

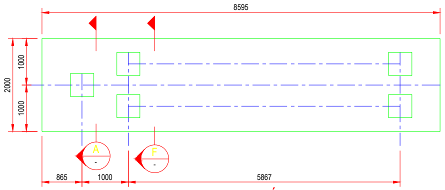

FUNDACIÓN
BANCO CAPACITADOR - 2160HF02
ESC. 1:50

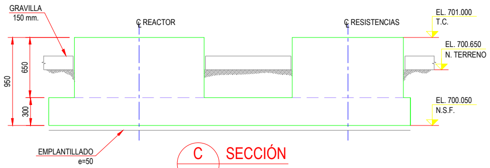

C SECCIÓN
ESCALA 1 : 25

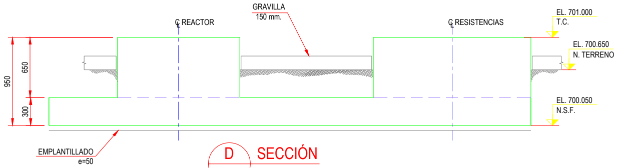

D SECCIÓN
ESCALA 1 : 25

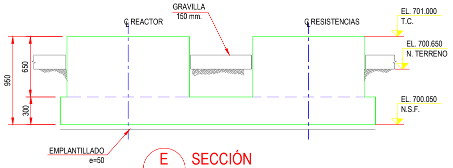

E SECCIÓN
ESCALA 1 : 25

CUADRO 1: CUBICACIÓN HORMIGONES (VER NOTA 8)

ÍTEM	VOLUMEN HORMIGÓN H25 EXISTENTE M^3	VOLUMEN HORMIGÓN G30 ADICIONAL M^3
HORMIGÓN FUNDACIÓN REACTOR/RESISTENCIA	17,6	3,5
FUNDACIÓN BANCO CAPACITORES	15,9	3,2
HORMIGÓN PÓRTICO DE LLEGADA	5,6	1,1
TOTAL	39,1	7,8

CUADRO 2: CUBICACIÓN EMPLANTILLADO (VER NOTA 7)

ÍTEM	VOLUMEN HORMIGÓN H05 EXISTENTE M^3	VOLUMEN HORMIGÓN G05 ADICIONAL M^3
HORMIGÓN EMPLANTILLADO REACTOR/RESISTENCIA	1,7	0,3
HORMIGÓN EMPLANTILLADO BANCO CAPACITORES	2,2	0,4
HORMIGÓN EMPLANTILLADO PÓRTICO DE LLEGADA	0,3	0,1
TOTAL	4,2	0,8

CUADRO 3: CUBICACIÓN ACEROS (VER NOTA 9)

ÍTEM	VALOR	UNIDAD
ACERO DE REFUERZO A630-420H	390	kg
PERNO POST INSTALADO Ø3/4" + VARILLAS HAS-E-55 + ADHESIVO HIT-RE-500-V3	216	un
PLACA BASE PL 12mm ASTM-A36 / A250ESP	174	kg

NOTAS:

1. DIMENSIONES EN mm , ELEVACIONES EN m.
2. LAS FUNDACIONES INDICADAS EN ESTE PLANO CORRESPONDEN A ESTRUCTURAS EXISTENTES, Y REFLEJAN EXCLUSIVAMENTE LA CONDICIÓN ACTUAL DE LAS FUNDACIONES DE LOS FILTROS ARMÓNICOS 23kV DE LAS SUBESTACIÓN PRINCIPAL.
3. MATERIALES:
   - HORMIGÓN EXISTENTE H25.
   - ACERO REFUERZO EXISTENTE A44-28H.
4. RECUBRIMIENTOS EXISTENTES :
   - FUNDACIONES 50 mm.
   - CARA INFERIOR FUNDACIONES 75 mm.
5. LOS EQUIPOS SUMINISTRADOS POR EL PROVEEDOR DEBEN CUMPLIR CON LOS CRITERIOS DE DISEÑO ESTABLECIDOS POR EL CLIENTE, DE ACUERDO CON LA NORMATIVA CHILENA VIGENTE.
6. LAS FUNDACIONES INDICADAS EN ESTE PLANO DEBERÁN SER VERIFICADAS DURANTE LA SIGUIENTE ETAPA DE INGENIERÍA DE DETALLES, EN FUNCIÓN DE LA INFORMACIÓN DEFINITIVA DE LOS EQUIPOS QUE SERÁN FINALMENTE INSTALADOS.
7. LOS EMPLANTILLADOS EXISTENTES QUE SE MUESTRAN SON DE CARÁCTER REFERENCIAL. DADO QUE NO SE CUENTA CON INFORMACIÓN VERIFICABLE DE ELLOS.
8. LAS CUBICACIONES DE LOS CUADROS 1 Y 2 CORRESPONDEN A LOS VOLÚMENES DE LAS ESTRUCTURAS EXISTENTES, ASÍ COMO A LOS NUEVOS REQUERIMIENTOS ESTRUCTURALES.
9. LAS CUBICACIONES PRESENTADAS EN EL CUADRO 3 CONSTITUYEN ESTIMACIONES REFERENCIALES, BASADAS EN LA GEOMETRÍA DE LAS FUNDACIONES EXISTENTES. ESTAS CIFRAS SON BASE PRELIMINAR PARA LA PLANIFICACIÓN DE SUMINISTROS, EL ANÁLISIS DE COSTOS (CAPEX) Y PROGRAMACIÓN DE OBRA.

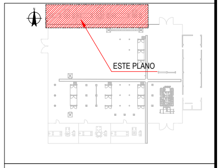

PLANO DE UBICACIÓN

REV.	REVISION / DESCRIPCION	FECHA	DIBUJO	DISEÑO	CHEQUEO	JEFE DISCIPLINA	INGENIERO PROYECTO	JEFE DE PROYECTO
Q	SIGUIENTE FASE	26/06/25	C.O.V.	F.G.L.	M.S.L.	F.P.C.	J.C.I.	M.V.V.
P	SIGUIENTE FASE	10/06/25	G.V.V.	F.G.L.	M.S.L.	F.P.C.	J.C.I.	M.V.V.
B	REVISIÓN CLIENTE	13/05/25	A.G.P.	F.G.L.	M.S.L.	F.P.C.	J.C.I.	M.V.V.
A	REVISIÓN INTERNA	24/04/25	A.G.P.	F.P.C.	M.S.L.	F.P.C.	J.C.I.	M.V.V.

N°	N° DE PLANO	PLANOS DE REFERENCIA	REV.
8			
7			
6			
5			
4			
3			
2	20P24012-G-160-EL-042-0002	DISPOSICIÓN DE EQUIPOS FASE 2	B
1	2160-C-201	PLANS, SECTIONS & DETAILS SHT1	4

APROBACION – INGENIERIA

	NOMBRE	FECHA	FIRMA
ADM. CONTRATO			
JEFE DE PROYECTO	M. VENENCIANO	26/06/25	
INGENIERO PROYECTO	J. CÁRDENAS	26/06/25	
JEFE DISCIPLINA	F. PROSSER	26/06/25	
CHEQUEO	M. SALAZAR	26/06/25	
DISEÑO	F. GODOY	26/06/25	
DIBUJO	C. OLIVERA	26/06/25	

GHD
Avda. A. Vespucio N° 100 Piso 9, Las Condes, Santiago, Chile
T 56 2 433 5400 F 56 2 918 2731
E ghdchile@ghd.com W www.ghd.com
www.ghd.com

Terminos de uso.
Este documento solo puede ser usado por el cliente de GHD (y/o por cualquier otra persona con la cual GHD hubiese acordado su uso) para el propósito que fue preparado, y no debe ser usado por ninguna otra persona ni para otro uso que no sea el especificado.

SUB–CONTRATO
CONTRATO MARCO 4600001025

Candelaria
lundin mining

APROBACION–CLIENTE

CLIENTE	FECHA
MAURICIO AVILÉS	26/06/25
N° PROYECTO	ESCALA
2000-PFS-24-012-OT 016	INDICADAS

N° PLANO CLIENTE
20P24012-G-2160-CI-066-0002

GHD S.A.

TITULO :
INGENIERÍA BÁSICA REEMPLAZO
FILTROS ARMÓNICOS 23KV, SUBESTACIÓN PRINCIPAL
PLANO
FUNDACIONES FASE 2

N° PLANO:
12658981-00000-CI-DRW-0002

REV.
Q

FORMATO – A1